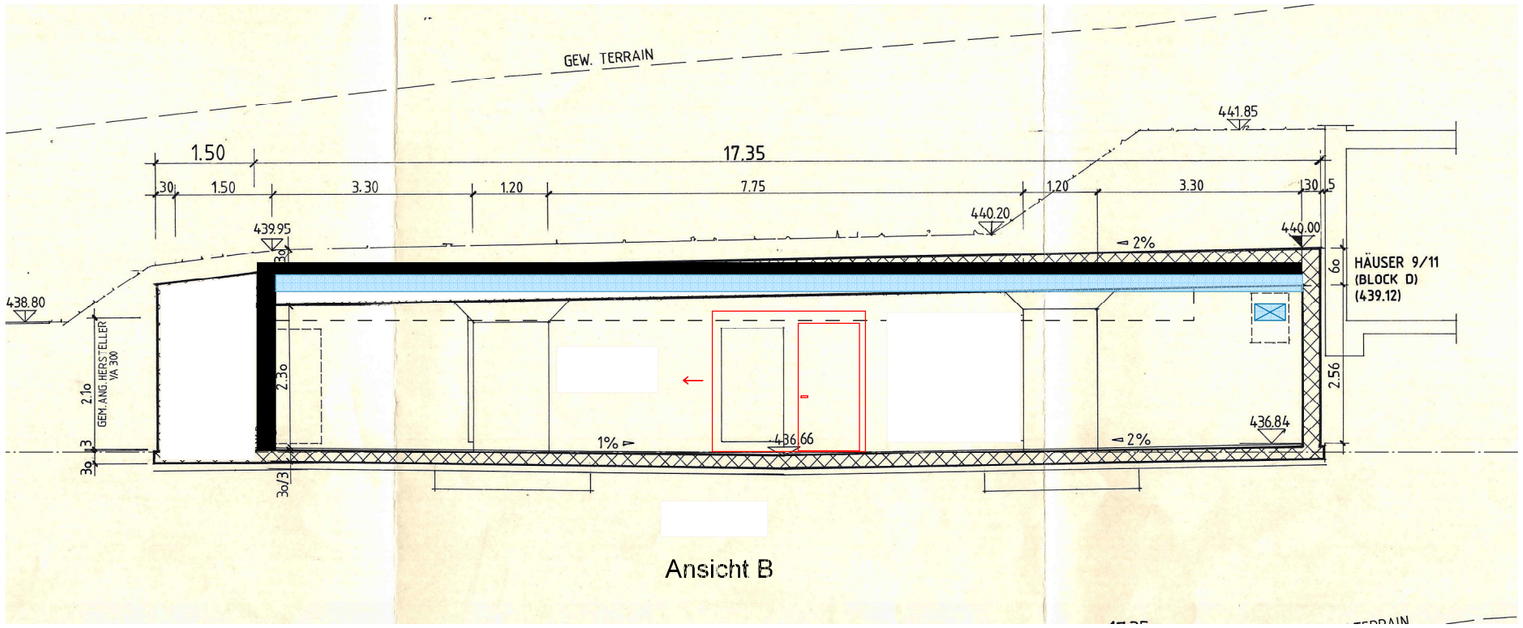

Ansicht B

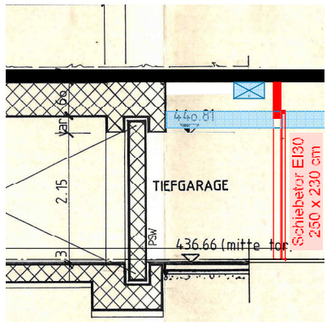

Schnitt A-A

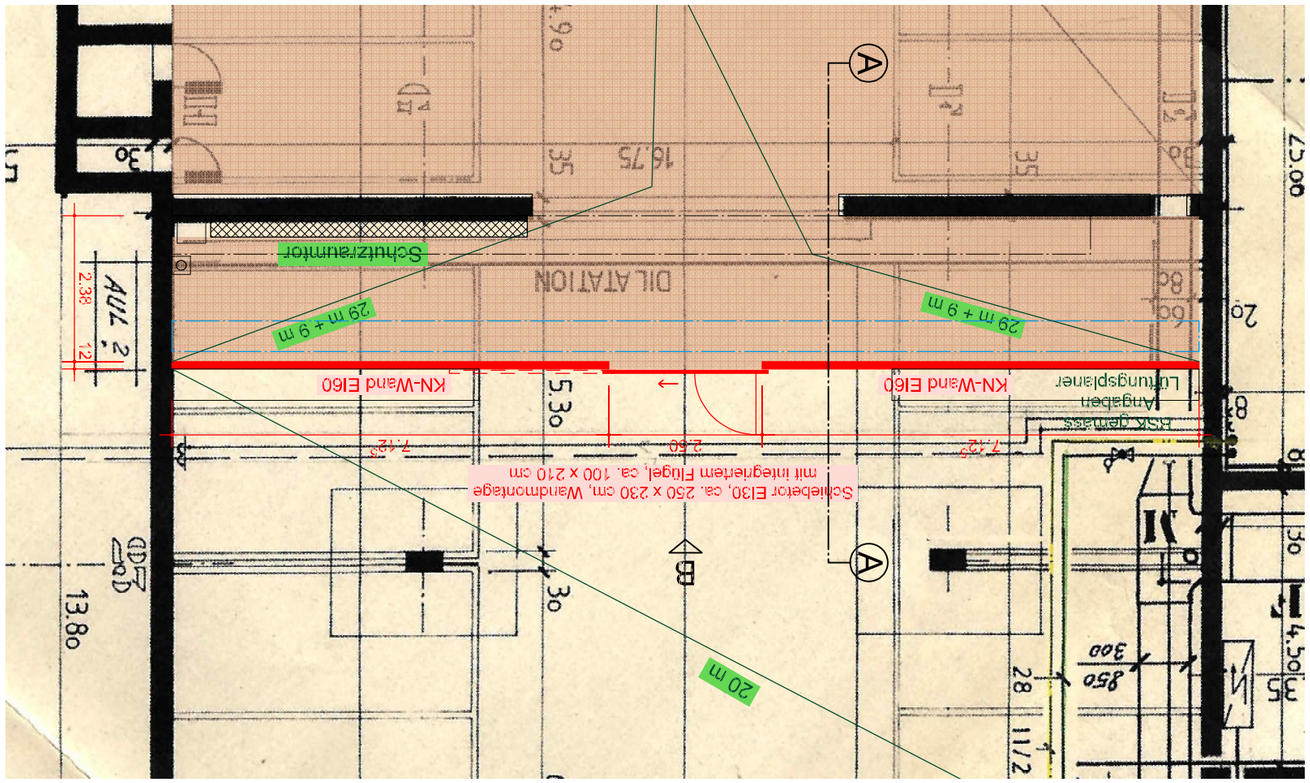

Grundriss

Kurzbeschrieb:

- Wand KN12 EI60 mit Sturz, da Boden und Decke im Gefälle
  Länge 2 x 712.5 cm + Sturz 250 cm
  Höhe var. ca. 289 cm
  Höhe Sturz var. ca. 60 cm
- Schiebetor ca. 250 x 230 cm, mit integrierter Flügeltüre, ca. 100 x 210 cm,
  Wandmontage, per Funk ansteuerbar oder per Schlüssel öffenbar
- Ausgleich bei Schwelle
- Anpassungen an Lüftung
- Abschottungen
- Demontage 2 FL-Röhren
- Ersatz Beleuchtung
- 2 neue Rettungszeichen sicherheitsbeleuchtet

Allreal Generalunternehmung AG
Lindbergh-Allee 1
8152 Glattpark
www.allreal.ch
allreal

Hohenstieglen 1 - 23
8152 Glattbrugg
Allreal Home AG
Objekt / Bauherr

Tiefgarage
Geschoss

Lagerraum anstatt
PP in Schutzraum
Planinhalt

1:100 / A3
Massstab / Format

20.08.2020 / GRI
Erstellt am / Gez.

26.08.2020 / GRI
Revidiert am / Gez.

Pfad Elite-Datei: P:\B_Hohenstiegeln_1-23_8152_Glattbrugg\02_Projekte\2020_Materiallager_Allreal\01_Studien
Pfad PDF-/ DWG-/ DXF-Dateien: W:\RU_allgemein\RU_PFM\Hohenstiegeln_1-23_8152_Glattbrugg\05_Planung\Architekt\01_Studien