Libs 5. OG Vega-Strasse 3 8152 Opfikon

424.40 M.ü.M. = +/- 0.00

BAUHERRHERRSCHAFT

Libs Industrielle Berufsrufslehre Schweiz
Thèrese-Gehse-Strasse 6
8050 Zürich

GRUNDEIGENTÜMER

Cornelia Hagmann
Chrapfstrasse 88
8126 Zumikon

ARCHITEKTUR & INNENARCHITEKTUR

Rubertone GmbH Design Concept
Ralph und Lino Grieco
Bergstrasse 63c
8712 Stäfa
Info@designconcept.ch

OBJEKTADRESSE

Vega-Strasse 3
UG - EG - 5.OG - 6.OG
8152 Opfikon - Glattbrugg

Legende

- Bestehend
- Neu
- Abbruch

Vorprojekt

5. Obergeschoss Grundriss

Massstab:	1:50
Plan-Nummer:	Libs_H113_5OG_v3
Plan-Format:	30cm x 84cm
Datum:	29. September 2020
Revision:	
Zeichner:	R.Grieco

Raumnummer 5-001	Raumnummer 5-002
Abstellraum 01 Boden: Doppelboden Wände: Abrieb/ Platten Decke : Beton roh BF 4 m2 PVC	Abstellraum 02 Boden: Doppelboden Wände: Abrieb Decke : Beton roh BF 4 m2 PVC

Raumnummer 5-003
Arbeitsraum Boden: Doppelboden Wände: Abrieb Decke : Beton roh BF 225 m2

Raumnummer 5-004
Bereichsleiter Boden: Doppelboden Wände: Abrieb Decke : Beton roh 14 m2

Raumnummer 5-005
Garderobe LE Herren Boden: Doppelboden Wände: Abrieb Decke : Beton roh BF 28 m2

Raumnummer 5-006
Garderobe Frauen Boden: Doppelboden Wände: Abrieb Decke : Beton roh BF 13 m2

Raumnummer 5-007
Garderobe Ausbilder Boden: Doppelboden Wände: Abrieb Decke : Beton roh BF 13 m2

Raumnummer 5-008	Raumnummer 5-009
Dusche Herren Boden: Doppelboden Wände: Abrieb Decke : Beton roh BF 4 m2	Dusche Frauen Boden: Doppelboden Wände: Abrieb Decke : Beton roh BF 4 m2

Raumnummer 5-010
Montage Boden: Doppelboden Wände: Abrieb Decke : Beton roh BF 68 m2

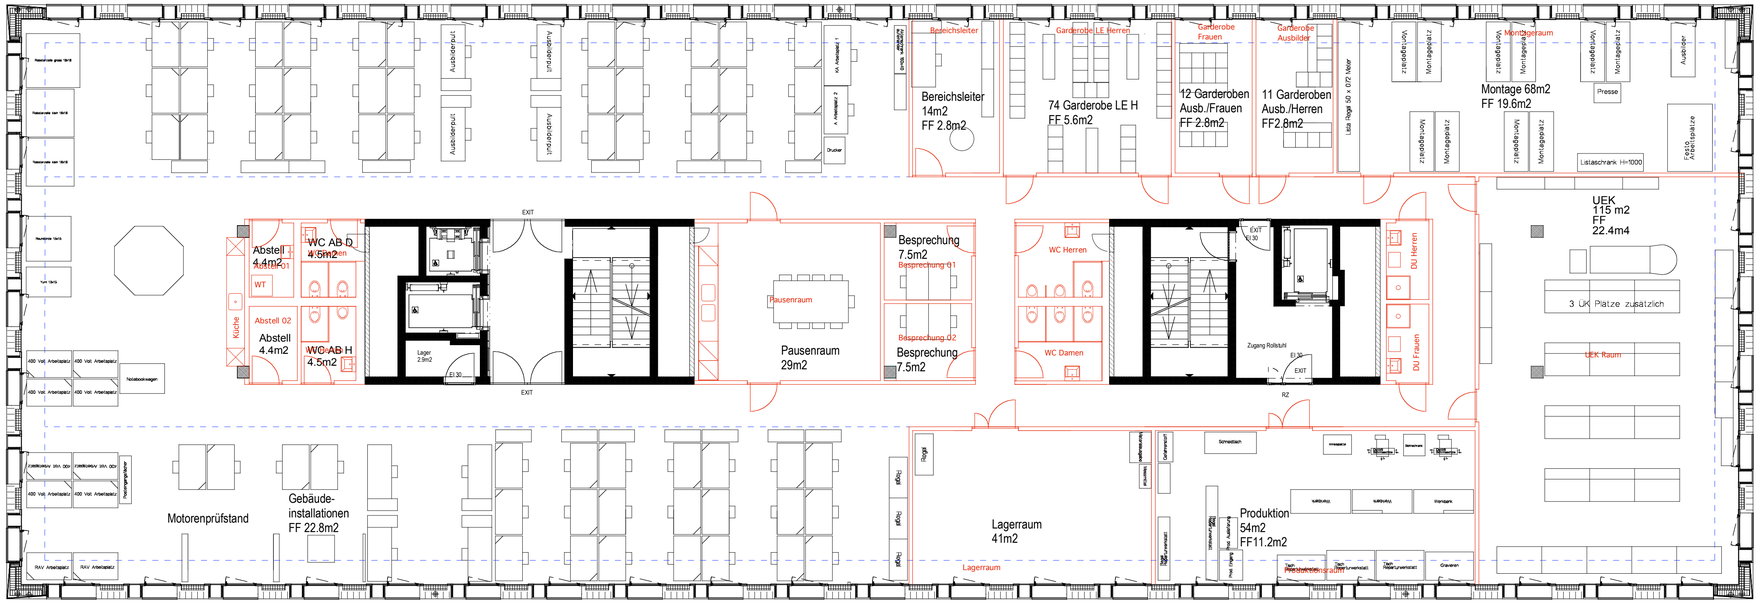

5. Obergeschoss

Raumnummer 5-021	Raumnummer 5-020
WC Herren Boden: Doppelboden Wände: Platten Decke : Beton roh BF 5 m2 PVC	WC Damen Boden: Doppelboden Wände: Platten Decke : Beton roh BF 5 m2 PVC

Raumnummer 5-019
Arbeitsraum Boden: Doppelboden Wände: Abrieb Decke : Beton roh BF 225 m2

Raumnummer 5-018
Pausenraum Boden: Doppelboden Wände: Abrieb Decke : Beton roh BF 29 m2

Raumnummer 5-017	Raumnummer 5-016
Besprechung 01 Boden: Doppelboden Wände: Abrieb Decke : Beton roh BF 7 m2	Besprechung 02 Boden: Doppelboden Wände: Abrieb Decke : Beton roh BF 7 m2

Raumnummer 5-015
Lager Boden: Doppelboden Wände: Abrieb Decke : Beton roh BF 54 m2

Raumnummer 5-014	Raumnummer 5-013
WC Herren Boden: Doppelboden Wände: Platten Decke : Beton roh BF 10 m2 PVC	WC Damen Boden: Doppelboden Wände: Platten Decke : Beton roh BF 9 m2 PVC

Raumnummer 5-012
Produktion Boden: Doppelboden Wände: Abrieb Decke : Beton roh BF 54 m2

Raumnummer 5-011
UEK Boden: Doppelboden Wände: Abrieb Decke : Beton roh BF 115 m2