Libs 5. OG Vega-Strasse 3

8152 Opfikon

424.40 M.ü.M. = +/- 0.00

BAUHERRHERRSCHAFT

Libs Industrielle Berufsrufslehre Schweiz Thèrese-Gehse-Strasse 6 8050 Zürich

GRUNDEIGENTÜMER

Cornelia Hagmann Chrapfstrasse 88 8126 Zumikon

ARCHITEKTUR & INNENARCHITEKTUR

Rubertone GmbH Design Concept Ralph und Lino Grieco Bergstrasse 63c 8712 Stäfa Info@designconcept.ch

OBJEKTADRESSE

Vega-Strasse 3 UG - EG - 5.0G - 6.0G 8152 Opfikon - Glattbrugg



Vorprojekt

5. Obergeschoss Grundriss

Massstab:	1:50
Plan-Nummer:	Libs_H113_50G_v3
Plan-Format:	30cm x 84cm
Datum:	29. September 2020
Revision:	
Zeichner:	R.Grieco

BF 4 m2 PVC

Boden: Doppelboden
Wände: Platten
Decke: Beton roh

BF 5 m2 PVC


BF 5 m2 PVC

BF 5 m2 PVC

Boden: Doppelboden Wände: Abrieb Decke: Beton roh BF 225 m2

Boden: Doppelboden Wände: Abrieb Decke: Beton roh BF 68 m2

Boden: Doppelboden Wände: Abrieb Decke : Beton roh BF 115 m2

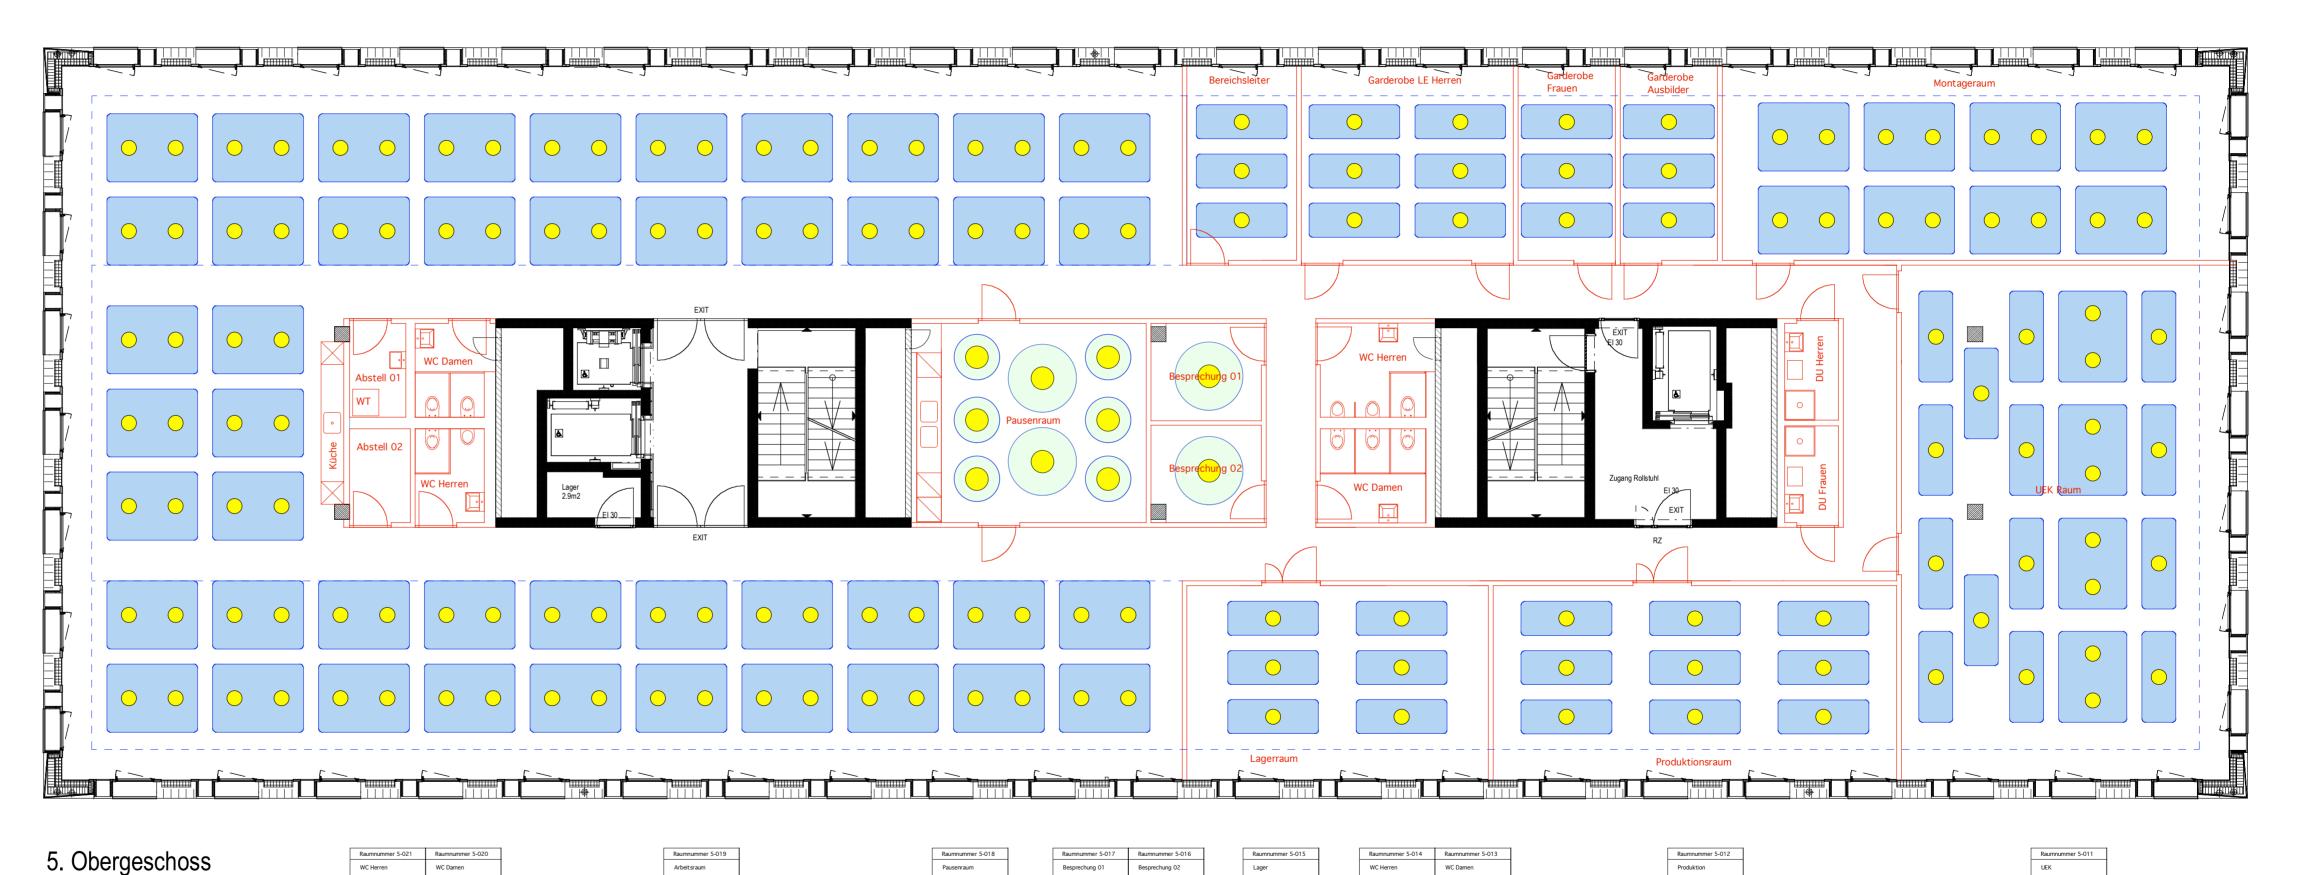

Besprechung 02

Boden: Doppelboden Wände: Abrieb Decke: Beton roh